


Approved

Surveyor General.

SV808F30

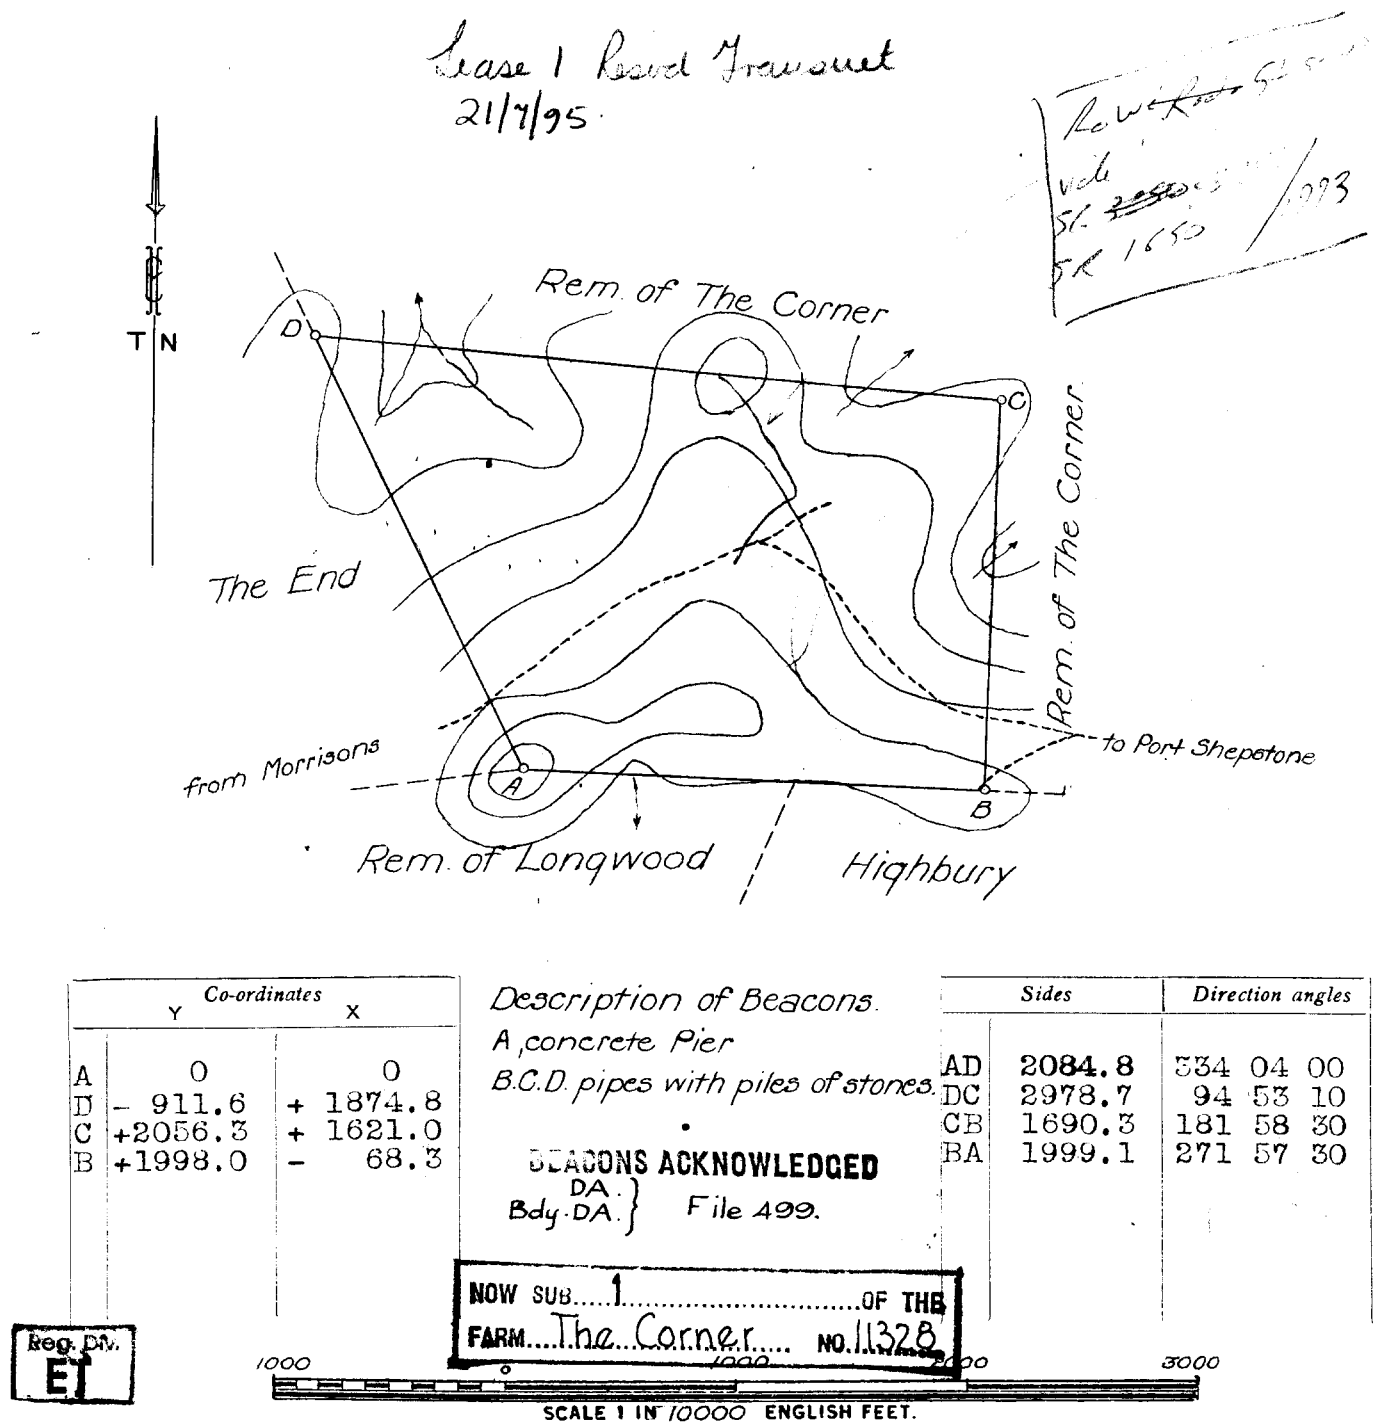

The figure A B C D
of land called

Represents 100 Acres ——— Square Feet

Sub. A of The Corner N^o 11328.

situate in the County of ALEXANDRA Province of Natal

Surveyed in June 1930. by me

S

C. R. Bullock

Land Surveyor

This diagram is annexed to deed of Transfer
No. 3278/1930
Dated 19 September 1930

Original diagram is annexed to
Deed of Grant No. 11328
Dated 6. Feb. 1929

(Sgd) H. Bezuidenhout
Registrar Deeds

Sub. Vol. 411

Fol. 1 ETSH
ETSC

COMP + T & A P. T. 9